
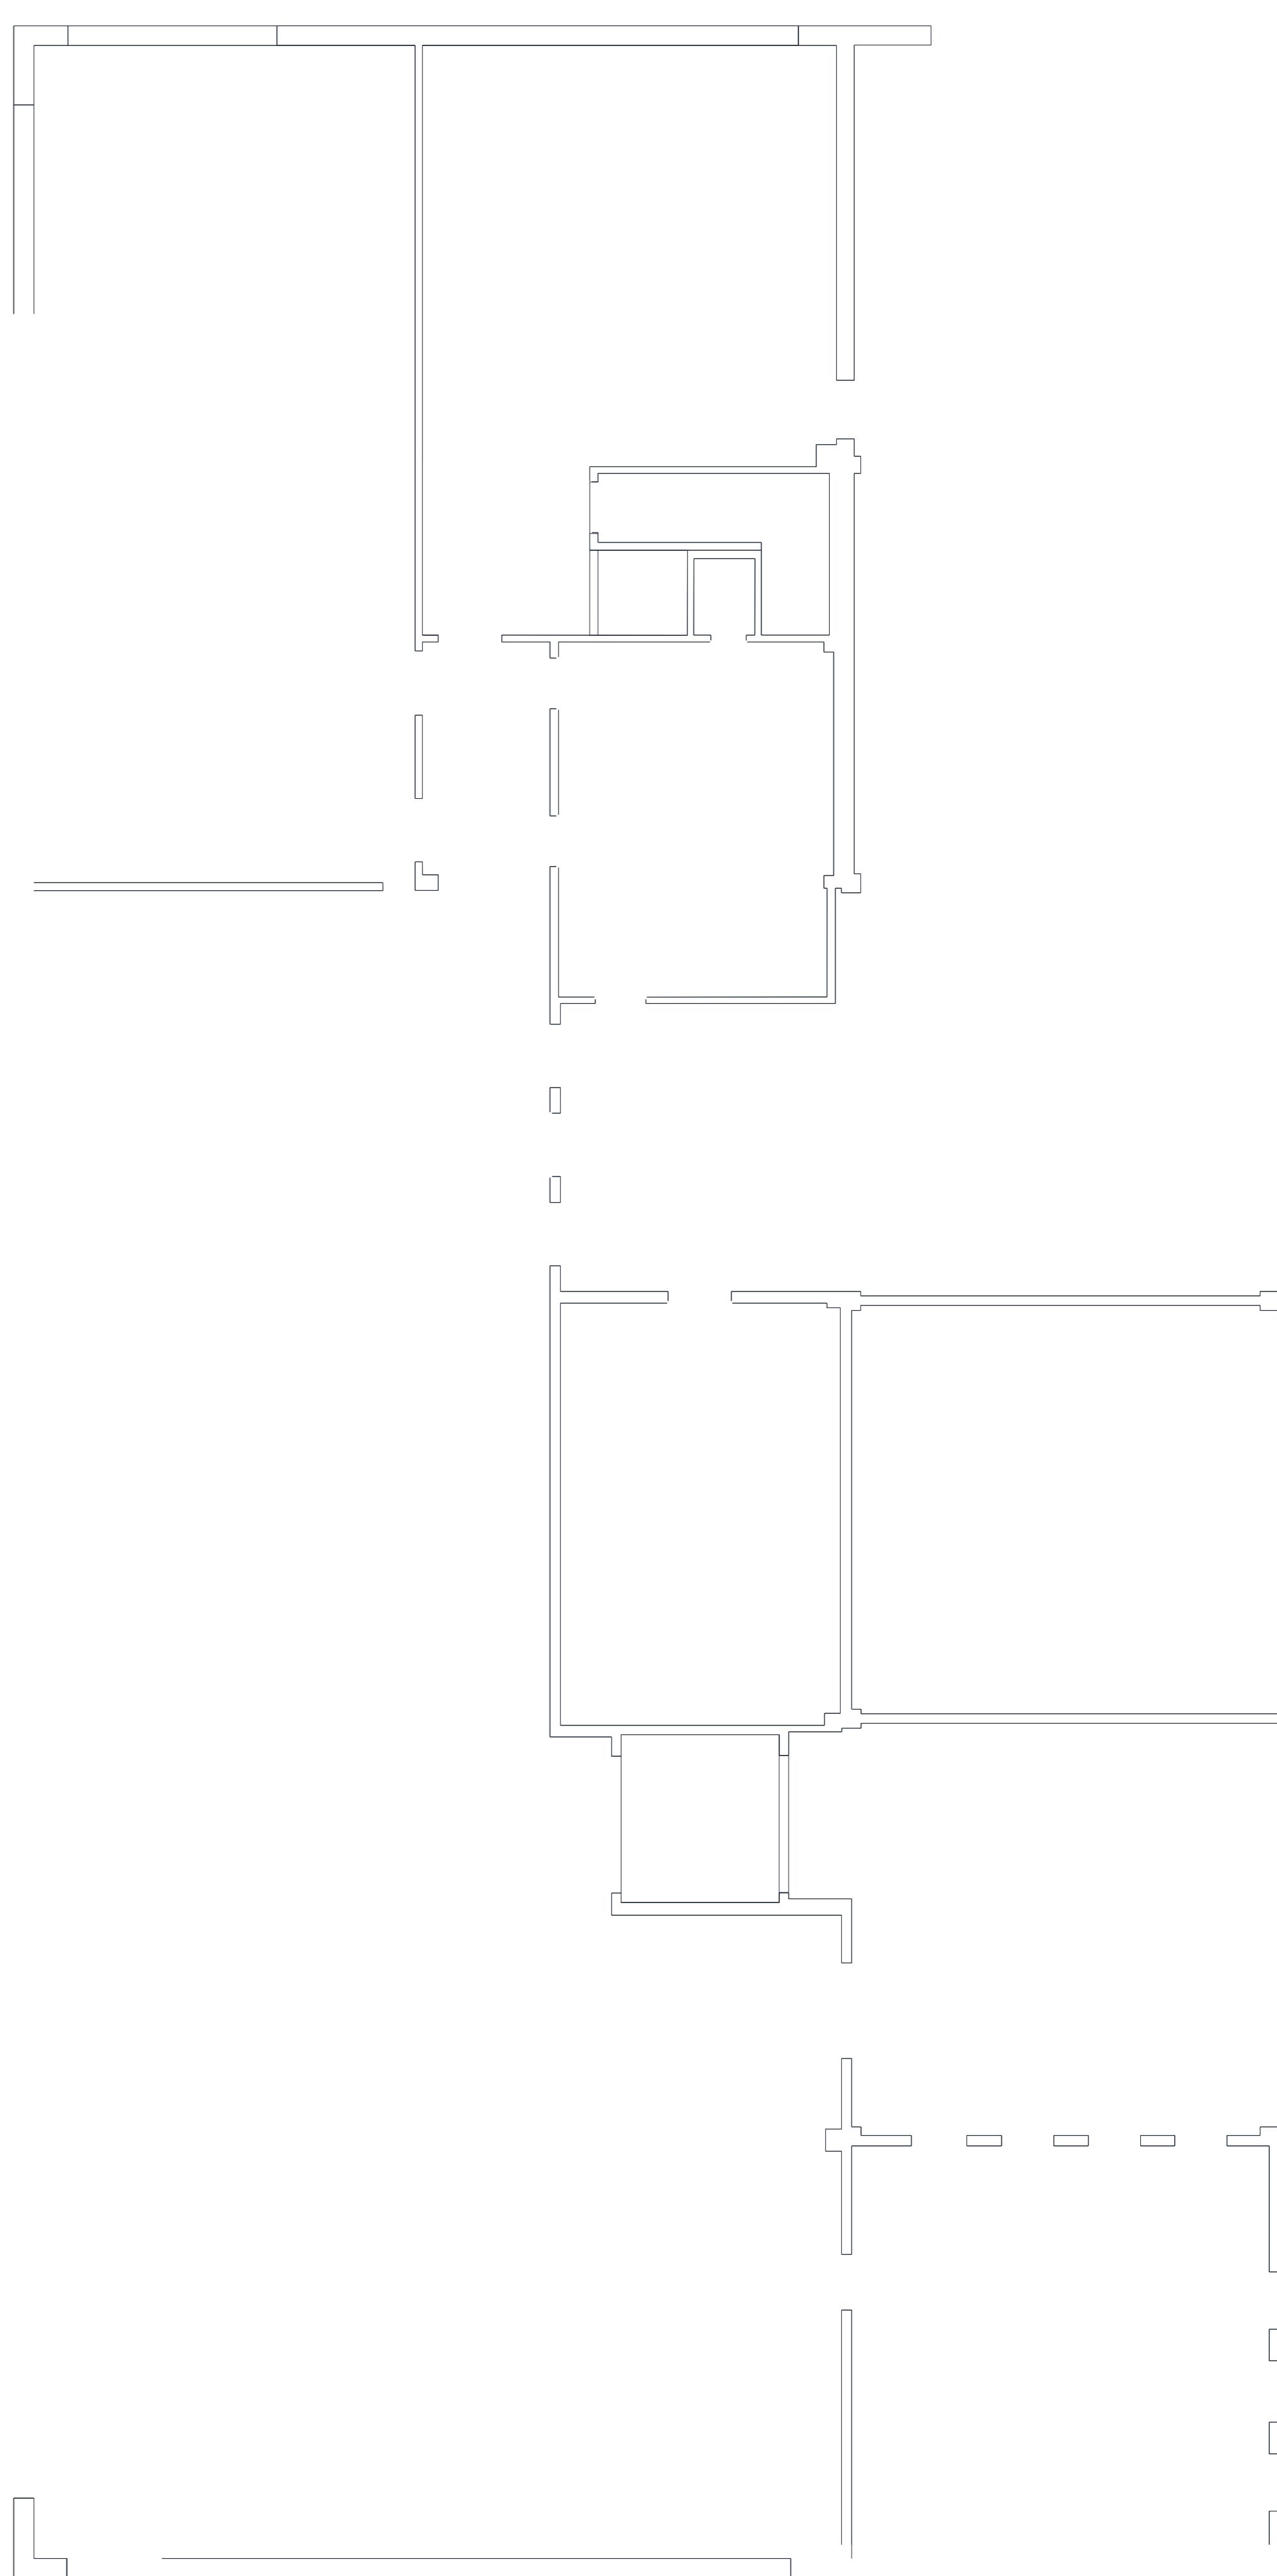


N

LÉGENDE
— Limite de box
— Circulation

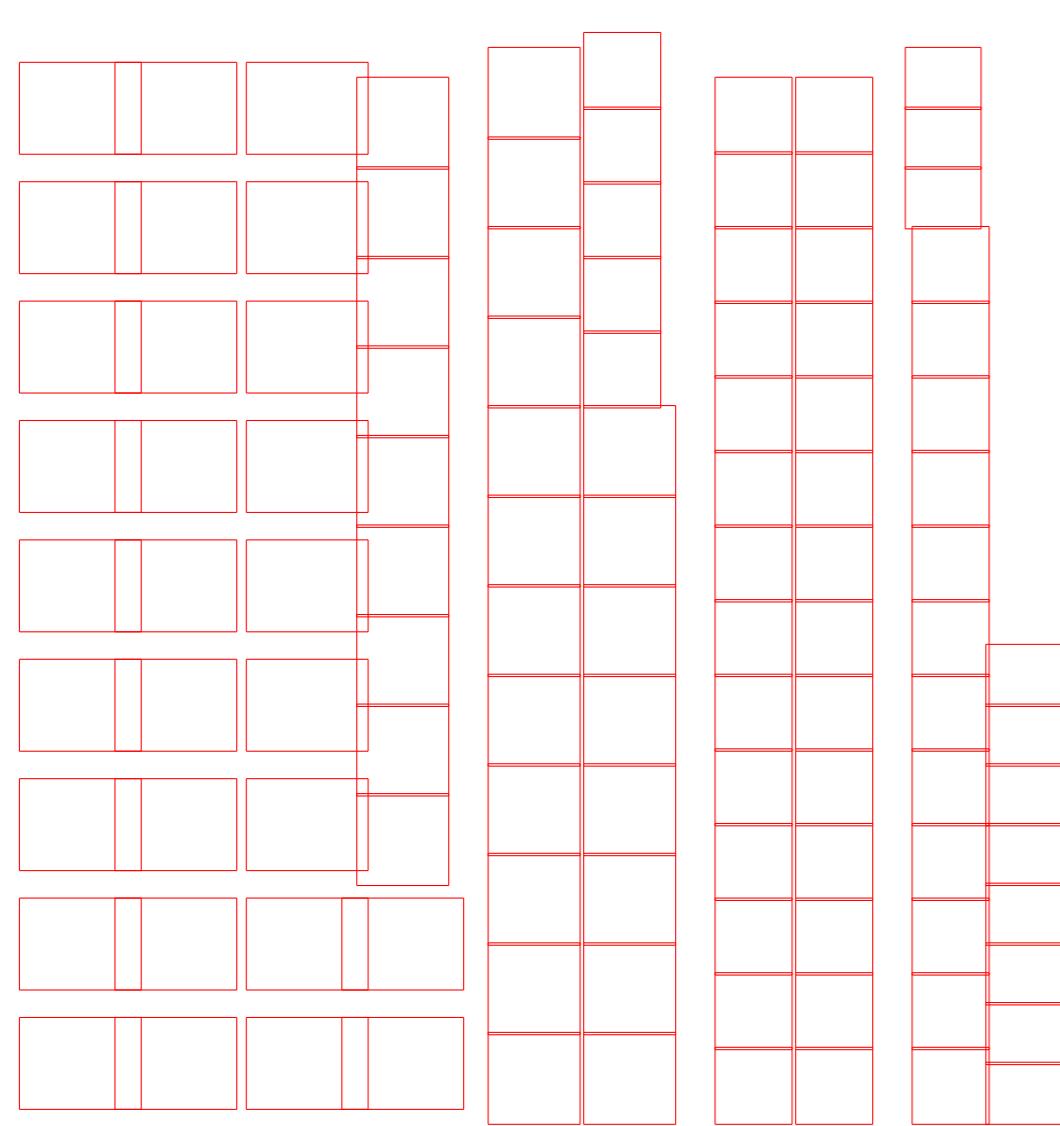

SURFACES DES BOX
 Nombre total: 114 boxes
 Surface totale: 90.49 m²

COSTO Layout
 Échelle 1:200